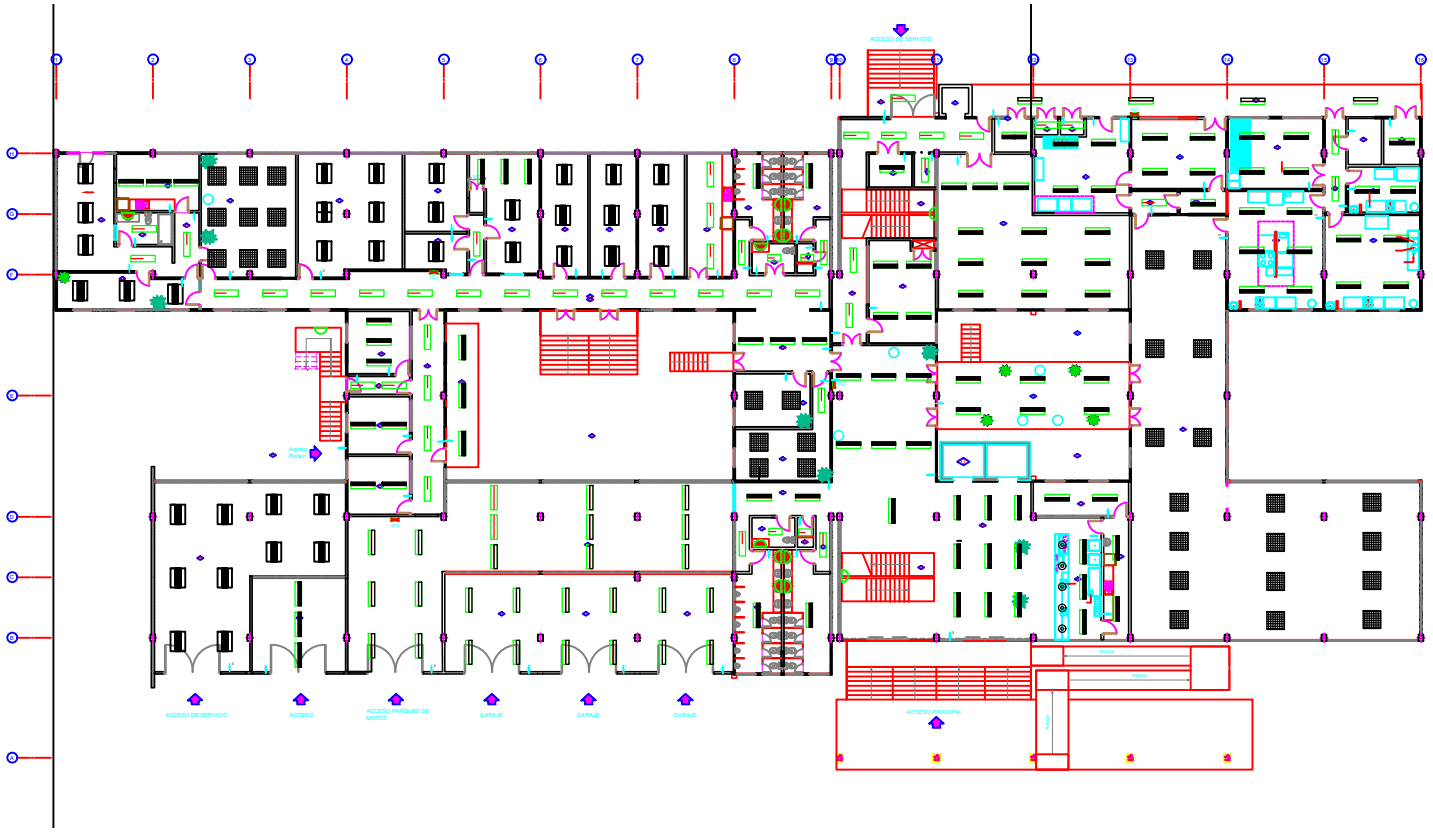


Tabla de Áreas Propuestas Nivel 0.00

No.	Locales	Área (m²)
100	Recepción-Cafetería	158.14
101	Elevadores	12.88
102	Escalera Pública	12.50
103	Escalera de Servicio	12.69
104	Circulación de Servicio	39.83
105	SS Públicos Mujeres	16.74
106	SS Públicos Hombres	16.82
107	SS Públicos Discapacitados	5.50
108	CL	2.12
109	SS Mujeres	14.02
110	SS Hombres	13.98
111	SS Discapacitados	4.84
112	CL	1.83
113	Montacargas	4.13
114	Puerta Metálica	46.74
115	Local de corrientes debiles	24.92
116	PCD	5.47
117	CE	2.65
118	Exter SS Públicos	20.65
119	Restaurante	270.65
120	Cafeteria Barra	53.41
121	Cafeteria-Elaboración	41.75
122	Cafeteria-Almacén Diario	12.58
123	Patio Interior Público	39.27
124	Patio Interior Público	20.76
125	Escalera Acceso de Servicio	16.12
126	Andén	96.10
127	Almacén	60.86
128	Local de Desperdicios	4.81
129	Local de Desperdicios de Cocina	1.52
130	Local de Desperdicios de Cocina	1.48
131	Freganlo	30.62
132	Comedor de Trabajadores	25.14
133	Almacén Cocina	25.44
134	Cámara Fría Cocina	5.87
135	Vacios Retromático	6.56
136	Preparación Fría	12.40
137	Preparaciones	34.29
138	Cocción	43.28
139	Despacho	4.23
140	Circulación Cocina	3.96
141	Circulación Cocina	6.95
142	Circulación Administrativa	75.18
143	Exter Administrativo	22.61
144	Salón de Protocolo	14.12
145	Salón de Reuniones	23.96
146	Patio Interior Administrativo	185.13
147	Pantry	22.05
148	Oficina	21.59
149	Oficina	21.59
150	Oficina	22.05
151	Oficina Economía	27.86
152	Oficina Contabilidad	19.33
153	Caja	8.11
154	Oficina de Gestores de Proyectos	47.38
155	Salón de Reuniones	44.59
156	Pantry Presidencia	17.85
157	SS Presidencia	6.75
158	Presidencia	31.47
159	Secretaria Presidencia	18.65
160	Circulación Presidencia	6.09
161	Tecnico de Mantenimiento, Talleres	103.22
162	Acceso Individual a Presidencia	23.37
163	Redes	14.73
164	Circulación Redes	29.62
165	Redes	11.64
166	Pesa de Redes	18.00
167	Redes	13.76
168	Escalera de Redes y Emergencias	29.78
169	Parqueo Motos y Ciclos	155.27
170	Parqueo Individual	36.73
171	Parqueo Individual	35.57
172	Parqueo Individual	35.52
173	Guardería de Mascotas. Pet Friendly	32.86
Total		1,942.58 m²

SIMBOLOGÍA

Interruptor sencillo 10 A 120 V en caja de empotrar de PVC de 104x68x50 mm a una altura de 1.2 mts del NPT0.

Interruptor doble 10 A 120 V en caja de empotrar de PVC de 104x68x50 mm a una altura de 1.2 mts del NPT0.

Interruptor doble 10 A 120 V en caja de empotrar de PVC de 104x68x50 mm a una altura de 1.2 mts del NPT0.

1x17 W 230 V 60 HZ

2x17 W 230 V 60 HZ — Luminaria para lámpara recta led para montaje empotrado en falso techo.

1x9 W 230 V 60 HZ

2x17 W 230 V 60 HZ — Luminaria para lámpara recta led para montaje adosado a losa de techo.

3x17 W 230 V 60 HZ — Luminaria para lámpara recta led para montaje empotrado en falso techo.

Luminaria decorativa bombillo led para montaje adosado en pared sobre los lavamanos en los baños con sistema offlon, apagado por presencia en 15 Minutos.

Luminaria circular para bombillo fluorescente compacto para montaje empotrado en falso techo.

Luminaria rectangular led para montaje empotrado en falso techo,con regulación de iluminación.

Arq. Nora Varela Reyes		NEXOS	PROYECTO: Edificio Inteligente PCT Villa Clara
Ing. David Herrera Cabezas		Empresa Contratista General de Obras, Villa Clara	CONTENIDO: PLANTA DE LUMINARIAS Nivel 0.0
Ing. José Basilio Novaez Cabello			ESCALA: 1:100 FECHA: 16-12-2025
			DISCIPLINA: Electricidad PLANO No.: Ele-01 HOJA No.: 4

MEMORIA DESCRIPTIVA.

OBRA: EDIFICIO INTELIGENTE PCT VC

OBJETOS DE OBRA: NIVEL 0.0

ESPECIALIDAD: ELECTRICIDAD

PROPUESTA DE ILUMINACION

CERTIFICACION DE RESPONSALIBIDADES

ENTIDAD RESPONSABLE DEL PROYECTO:

NEXOS (ECGO Empresa Contratista General de Obras) de Santa Clara, Villa Clara.

FECHA DE ELABORACION

DICIEMBRE DEL 2025

EXPERTOS RESPONSABILIZADOS CON EL ESTUDIO POR NEXOS:

Especialista A en obras de Arquitectura José B Novaez Cabello

- Responsable del Proyecto

Especialista A en obras de Arquitectura Arq. Irina Varela Reyes

- Revisión del Proyecto

Director UGDC #6. Dagni Herrera Cabrera.

- Aprobación del Proyecto

Firma:_____

FUENTES DE PROCEDENCIA DE LA INFORMACION

- PLANO DE MOBILIARIO Y EQUIPOS NIVEL 0.0 ENTREGADO ESPECIALISTA DE ARQUITECTURA UGDC#6.
- CATALOGOS DE LUMINARIAS UTILIZADOS 3F FILIPPI, ARTEMIDE S.P.A, AURA LIGHT, SYLVANIA,
- SOFWARE DIALUX 4.13.02

Dado a los días 17 del mes de Diciembre del año 2025

Para realizar el análisis de iluminación evaluamos las necesidades para cada área y local y en base a ello definimos las luminarias más idóneas, para utilizar en cada área.

También en los locales donde se ubiquen más de 2 luminarias proponemos la utilización de interruptores dobles y triples para encender lo que sea realmente necesario.

PARA LAS AREAS DE ESTAR, OFICINAS, AULAS, PANTRY, SERVICIOS SANITARIOS, CLOSET Y LOS PASILLOS, SE PROPUSIERON LUMINARIAS RECTAS DE EMPOTRAR EN FALSO TECHO PARA LAMPARAS LED DE 1X9, 1X17 W Y 2X17 W.

AURA 81390095 Carlina LED Recessed 1x17/28W DALI /



PARA LAS ESCALERAS, SE PROPUSIERON LUMINARIAS DE ADOSAR EN PARED EN CADA PASO DE ESCALERA PARA LUMINARIAS LED DE 14 W

ARTEMIDE L2281190 Niki LED policarbonato 3000K lucido /



Clasificación luminarias según CIE: 99
Código CIE Flux: 45 76 94 99 100

Niki LED policarbonato 3000K lucido

EN LOS BAÑOS ADEMAS DE LAS LUMINARIAS RED PARA LAMPARAS LED DE 1X17, SE PROPONE LAL UTILIZACIÓN SOBRE LOS LAVAMANOS DE APLIQUES CON SENSOR OFF/ON QUE SE PUEDE PROGRAMAR PARA ENCENDER Y APAGAR EN 15 Y HTA 30 MINUTOS SIN PRESENCIA, PARA LAMPARAS LED DE 14 W

AURA 7362.311.07 Elim LED 3000K Sensor on/off /



Clasificación luminarias según CIE: 49
Código CIE Flux: 15 39 68 49 101

APPLICATIONS:
Public areas, entrances, offices, corridors.

MATERIAL: Luminaire frame of grey lacquered steel plate and screen by matting, opal plexiglass.

INSTALLATION AND CONNECTION:
Cable entry from the top, the bottom and from the back. Terminal block 2,5 mm 2 .

TECHNICAL DATA:
220-240V, 50-60Hz, IP20. Power factor >0,9. Ambient temperature +0 - +25° C. CE. Lifetime 50.000 hours (L70B50). 3000K and 4000K, CRI >80. LED module MacAdam 3 SDCM. DSI. Analog dimming 1-10V. Phase pulse control. HF SENSOR – On/off 15 min. Time 15 min is set from the factory and can be changed in different stages from 1-30 min. Profile 1 with maximum level 100% in 15 min and minimum level 10% by absence. Profile 2 with maximum level 100% in 15 min and minimum level 10% by absence for 30 min, then off to the next presence detection.

PARA LOS SALONES DE PROTOCLOS, REUNIONES Y CONFERENCIAN QUE PRECISAN DE UN ALTO NIVEL DE ILUMINACION SEGÚN NORMA, SE PROPONE LA UTILIZACIÓN DE LUMINARIAS LED DE 40 WATT EMPOTRABLES Y REGULABLES, LO QUE PERMITE DISMINUIR LA LUMINOSIDAD, PARA VER DIAPOSITIVAS O DURANTE UNA VIDEOCONFERENCIA Y ADEMAS COMO SON LOCALES GARNDES CON GRAN CAPACIDAD DE PERSONAS SE COLOCARAN INTERRUPTORES

DOBLES Y TRIPLES PARA NO ENCENDER LAS LUMINTARIAS INNECESARIAMENTE.

3FFILIPPI 23848 3F Diagon 39W/930 DALI SOFT UGR 621x621



Clasificación luminarias según CIE: 100
Código CIE Flux: 59 92 99 100 100

CARACTERÍSTICAS LUMINOTÉCNICAS
Rendimiento luminoso 100% (DLOR 100%, ULOR 0%).
Flujo luminoso inicial de la luminaria 3890 lm.
Distribución directa simétrica.
Instalación de Interdistance Dtransv. = 1,23 x hu - Dlong. = 1,23 x hu.
Luminancia media <3000 cd/m² para ángulos >65° radiales.
UGR <19 (EN 12464-1).
Eficacia luminosa 97 lm/W.
Duración útil (L90/B10): 30000 h. (tq+25°C)
Duración útil (L85/B10): 50000 h. (tq+25°C)
Duración útil (L80/B20): 80000 h. (tq+25°C)
Duración útil (L70/B20): 100000 h. (tq+25°C)
Disminución repentina del flujo luminoso después de 50000 h: 0% (C0).
Seguridad fotobiológica conforme a la norma IEC/TR 62778: (RG0) (IEC 62471).
Conforme a las normas IEC/EN 62722-2-1 - IEC/EN 62717.

FUENTE
Módulo de LED cuadrado 39W/930.
Clase de eficiencia energética: E.
Índice de reproducción cromática CIE 13.3: CRI >90 (R9 >50%).
Índice de Fidelidad cromática IES TM-30: Rf = 92 Rg = 101.
Temperatura nominal de color CCT 3000 K.
Tolerancia de color inicial (Mac Adam): SDCM 3.

APLICACIONES
Salas de conferencia, con videoterminales, oficinas.
Ambientes con tareas visualmente demandantes, donde es necesaria una iluminación difusa y suave para un óptimo confort visual.

GESTIÓN DE LA LUZ
El dispositivo, equipado con el controlador DALI, puede controlarse manualmente con la tecnología 3F Easy Dim o automática / manualmente con la tecnología 3F Smart Dimming.
En sistemas eléctricos sin un sistema de regulación (manual o automático), se debe hacer un puente adecuado en los terminales DA-DA del aparato.

EN EL LOCAL DE RECEPCION DE HOSPEDAJE ADEMAS DE LA ILUMINACION NORMAL CON LUMINARIAS RECTAS CON LAMPARAS LED DE 2X17 W, PROPONEMOS LA COLOCACIÓN SOBRE EL AREA DE LA BARRA DE LUMINARIAS CIRCULARES EMPOTRADAS EN EL TECHO SOBRE LA MISMA CON LUMINARIAS FLUORESCENTES COMPACTAS DE 22 W.

Artemide M115050 ANDROMEDA EMPOTRADO 300X300MM T16-R 1X22W




Clasificación luminarias según CIE: 85
Código CIE Flux: 40 71 90 85 22


ANDROMEDA EMPOTRADO 300X300MM T16-R 1X22W + HIR111 MAX.1X35W

EN ESTE NIVEL CONSIDERAMOS PARA LAS OFICINAS Y EL AREA PRESIDENCIAL LA UTILIZACIÓN DE LUMINARIAS DE 3X18 PARA MONTAJE EMPOTRADO CON SENSOR DE TEMPERATURA.

AURA 81365640 Concelo 3 x 17 W DALI Sensor / Hoja de datos de luminarias

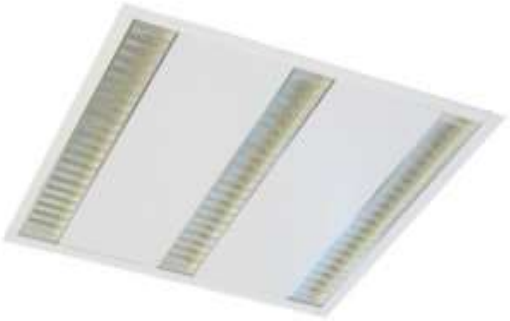

Emisión de luz 1:

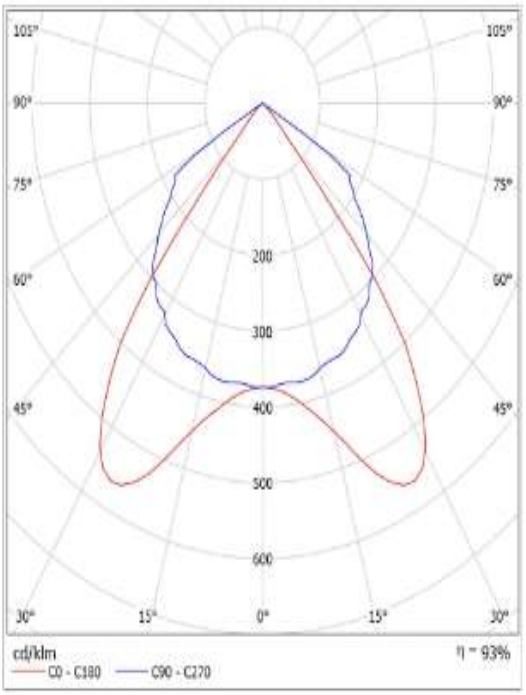

Clasificación luminarias según CIE: 100
Código CIE Flux: 73 99 100 100 93

Para esta luminaria no puede presentarse ninguna tabla UGR porque carece de atributos de simetría.

APPLICATIONS:
Offices, schools, shops, meeting areas.

MATERIAL:
Housing made of sturdy galvanised sheet steel, white powder coated. Double parabolic reflectors in semi-diffuse (MIRO5 Silver) aluminum. Aura Concelo uses spring fixed louvres for safe, quick installation and maintenance.

INSTALLATION AND CONNECTION:
Aura Concelo is designed for recessed mounting in suspended ceiling 600 mm or 1200 mm grid, with visible T-bars. Delivered with 2 m 5-pole cable. Can also be supplied with Wieland or Winsta connector or 2,5 m mains cable and earthed plug.

COMPONENTS:
Aura UltiLED Long Life, 3x8 W or 2x17 W, 3000K or 4000K. Dimmable DALI 2-channel LED driver, 350mA 3x8W or 700mA 2x17W. Intelligent Temperature Guard gives protection against thermal damage. Light sources must be ordered separately.


TECHNICAL DATA:
220V-240V 50-60 Hz, Class I, IP20, CE.

Y PARA LAS AREAS DE SE PROPUSIERON LUMINARIAS RECTAS PARA ADOSAR A LA LOSA DEL TECHO PARA LAMPARAS LED DE2X17 W.

AURA 5137.202.00 Z44 2x17W UltiLED / Hoja de datos de luminarias



Emisión de luz 1:

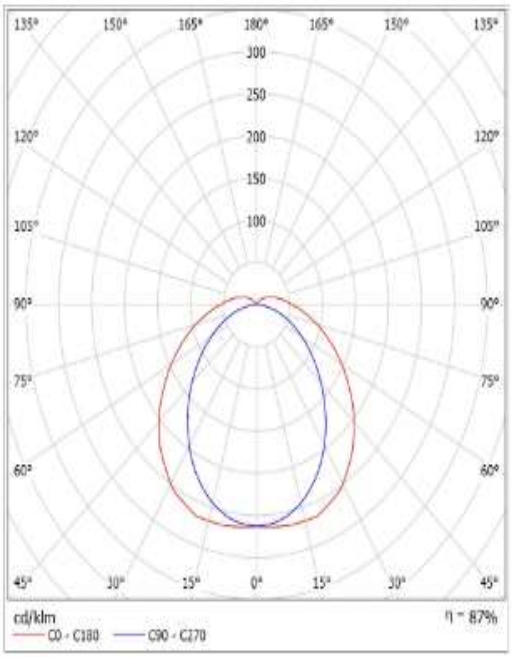

Clasificación luminarias según CIE: 93
Código CIE Flux: 44 74 91 93 88

APPLICATIONS:
Corridors, industries, workshops, storage rooms, culverts, kitchens and laboratories.

MATERIAL:
Housing made of white painted steel with end caps in molded ASA plastic. Frosted, prismatic cover of extruded acrylic plastic.

INSTALLATION AND CONNECTION:
Ceiling mounted IP44 or wall IP20. Ø 20 mm cable entry in both end caps and 2 Ø 19 mm cable entries in the center of the luminaire. 5x2,5 mm² terminal block.

COMPONENTS:
Light source: Aura UltiLED Long Life 3000K or 4000K, 1x8 W, 2x8 W, 1x17 W, 2x17 W, 1x23 W or 2x23 W. Lifetime (L80B10) 58 000 hours. For more information see separate product sheet. Note that light sources must be ordered separately. Control gear: Non-dimmable or DALI dimmable LED driver, 350 mA for 8 W and 700 mA for 17 W and 23 W UltiLED Long Life versions. Sensor: HF sensor with settings for detection range, delay time and lux on / lux off value.

TECHNICAL DATA:
220 - 240V, 50-60 Hz, class I, IP44 (IP20 for wall mount). Power factor λ > 0,95 Ambient temperature: -25° to +25°C. CE.

Emisión de luz 1:

Valoración de deslumbramiento según UGR

ρ Techo		70	70	50	50	30	70	70	50	50	30
ρ Paredes		50	30	50	30	30	50	30	50	30	30
ρ Suelo		20	20	20	20	20	20	20	20	20	20
Tamaño del local X	Y	Mirado en perpendicular al eje de lámpara					Mirado longitudinalmente al eje de lámpara				
2H	2H	23.8	25.1	24.2	25.5	25.8	21.1	22.4	21.5	22.8	23.1
	3H	26.0	27.1	26.4	27.5	27.9	22.3	23.5	22.7	23.9	24.3
	4H	27.1	28.2	27.5	28.6	29.0	22.8	23.9	23.2	24.3	24.7
	6H	28.3	29.3	28.7	29.7	30.2	23.1	24.1	23.6	24.6	25.0
	8H	28.9	29.9	29.4	30.3	30.8	23.2	24.2	23.7	24.6	25.1
	12H	29.6	30.6	30.1	31.0	31.5	23.2	24.2	23.7	24.6	25.1
4H	2H	24.3	25.4	24.7	25.8	26.2	22.3	23.4	22.7	23.8	24.2
	3H	26.7	27.7	27.2	28.1	28.6	23.7	24.7	24.2	25.1	25.6
	4H	28.0	28.9	28.5	29.4	29.9	24.3	25.2	24.8	25.7	26.2
	6H	29.5	30.2	30.0	30.7	31.2	24.8	25.5	25.3	26.0	26.6
	8H	30.2	30.9	30.8	31.4	32.0	24.9	25.6	25.5	26.1	26.7
	12H	31.1	31.7	31.6	32.2	32.8	25.0	25.7	25.6	26.2	26.8
8H	4H	28.3	29.0	28.8	29.5	30.1	25.2	25.9	25.8	26.4	27.0
	6H	30.0	30.6	30.6	31.1	31.7	26.0	26.6	26.6	27.1	27.7
	8H	31.0	31.5	31.5	32.0	32.6	26.3	26.8	26.9	27.4	28.0
	12H	32.1	32.5	32.7	33.1	33.7	26.5	27.0	27.1	27.5	28.2
12H	4H	28.3	29.0	28.9	29.5	30.1	25.5	26.1	26.1	26.7	27.2
	6H	30.1	30.6	30.7	31.1	31.8	26.4	27.0	27.0	27.5	28.1
	8H	31.1	31.6	31.7	32.2	32.8	26.9	27.3	27.5	27.9	28.6

Variación de la posición del espectador para espaciamientos S entre luminarias

S = 1.0H	+0.1 / -0.1	+0.1 / -0.1
S = 1.5H	+0.3 / -0.3	+0.2 / -0.4
S = 2.0H	+0.3 / -0.5	+0.4 / -0.7
Tabla extendida	8K10	8K14
Sumando de corrección	14.6	9.4

Índice de deslumbramiento corregido en relación a 1000lm Flujo luminoso total

Tabla de Luminarias Propuestas Nivel 0.00

No.	Locales	Área (m²)	LARGO M	ANCHO M	NIVELES DE ILUMINACION NORMA NC ISO 8995	NIVELES DE ILUMINACION ALCANZADO EN DIALUX	CANTIDAD	LUMINARIAS LINEALES LED EN WATT EMPOTRADAS	LUMINARIAS LED EN WATT
100	Recepción-Cafetería	158,1	9.75	5.8	200	233	8	2X17	
101	Elevadores	12,88							
102	Escalera Pública	12,50					1		1X14 CIRCULAR ADOSADA
103	Escalera de Servicio	12,69					1		1X14 CIRCULAR ADOSADA
104	Circulación de Servicio	39,83	6.84	2.15	100	103	2	1X17	
105	SS Público Mujeres	18,71	6	2.85	100	118	2	2X17	2 (1X14) DECORATIVA CON SENSOR ON/OFF
106	SS Público Hombres	18,82	6	2.85	100	118	2	2X17	2 (1X14) DECORATIVA CON SENSOR ON/OFF
107	SS Público Discapacitados	5,50	2.65	1.82	100	115	1	1X9	1 (1X14) DECORATIVA CON SENSOR ON/OFF
108	CL	2,12	1.82	1	100	120	1	1x9	
109	SS Mujeres	14,02	6	2.85	100	118	2	2X17	2 (1X14) DECORATIVA CON SENSOR ON/OFF
110	SS Hombres	13,98	6	2.85	100	118	2	2X17	2 (1X14) DECORATIVA CON SENSOR ON/OFF
111	SS Discapacitados	4,84	2.65	1.82	100	115	1	1X9	1 (1X14) DECORATIVA CON SENSOR ON/OFF
112	CL	1,83	1.82	1	100	120	1	1x9	
113	Montacargas	4,13							
114	Puente Metálico	46,71	12	4.1	200	200	6	2X17	
115	Local de corrientes debiles	24,92	6.35	4.1	300	230	4	2X17	
116	PGD	5,47	2.65	2.05	200	200	1	2X17	
117	CE	2,65	2.05	1.32	200	170	1	1x17	
118	Estar SS Públicos	20,65	6	1.9	200	210	2	2X17	
119	Restaurante sección 1	270,6	17.9	9.7	200	213	12	1x40 REG	
	Restaurante sección 2		16.5	5.9	200	200	6	1x40 REG	
120	Cafetería Barra	33,41	6.52	8.25	200	229	3	2X17	
	Barra		6.52	2.85	100	100	5		1X22 FLC CIRCULAR EMPOTRADO
121	Cafetería-Elaboración	11,75	7.56	1.55	200	200	2	2x17	
122	Cafetería-Almacén Diario	12,58	5.9	2.1	200	203	3	2x17	
123	Patio Interior Público	39,27							
124	Patio Interior Público	20,76							
125	Escalera Acceso de Servicio	18,12					1		2X17 ADOSADA
126	Andén	56,10	27.8	2	100	100	4	2x17	
127	Almacén sección 1	90,86	11.8	5.8	200	226	9	2x17	
	Almacén sección 2		5.9	3.8	200	203	3	2x17	
128	Local de Desperdicios	4,81	2.33	2.1	200	215	1	2x17	
129	Local de Desperdicios de Cocina	1,32	1.45	1	200	200	1	1X17	
130	Local de Desperdicios de Cocina	1,46	1.45	1	200	200	1	1X17	
131	Fregado	30,62	5.8	4.7	200	223	4	2X17	
132	Comedor de Trabajadores	25,14	5.9	4.3	200	236	4	2X17	
133	Almacén Cocina	25,44	5.9	4.3	200	236	4	2X17	
134	Cámara Fría Cocina	5,87	2.85	2	200				
135	Vacios Retornables	6,56	2.85	2.25	200	185	1	2X17	
136	Preparación Fría	12,40	2.85	2.83	200	214	2	2X17	
137	Preparaciones	34,29	5.9	5.8	200	200	4	2X17	
138	Cocción	43,28	7.3	5.9	200	225	6	2X17	
139	Despacho	4,23	2.88	1.4	200	226	1	2X17	
140	Circulación Cocina	3,96	2.88	1.4	100	133	1	1X17	

141	Circulación Cocina	6,95	5.8	1.3	100	148	1	1X17	
142	Circulación Administrativa	78,18	38.9	1.85	100	103	10	1X17	
143	Estar Administrativo	22,81	5.9	3.75	200	224	6	2X17	
144	Salón de Protocolo	14,12	4.62	3.3	500 Reg	316	2	1x40 REG	
145	Salón de Reuniones	23,96	5.9	3.18	500 Reg	500	4	1x40 REG	
146	Patio Interior Administrativo	165,1							
147	Pantry	22,35	7.6	2.9	200	200	3	1X17	
148	Oficina	21,59	7.6	2.9	300	369	3	3X17	
149	Oficina	21,59	7.6	2.9	300	369	3	3X17	
150	Oficina	22,35	7.6	2.9	300	369	3	3X17	
151	Oficina Economía sec 1	27,86	5.25	3.3	300	317	2	3X17	
	Oficina Economía sec 2		4.35	2.15	300	377	3	2X17	
152	Oficina Contabilidad	19,33	4.8	3.85	300	303	3	3X17	
153	Caja	8,11	3.85	2.2	300	300	1	3X17	
154	Oficina de Gestores de Proyectos	47,38	7.2	6.45	300	381	6	3X17	
155	Salón de Reuniones	44,59	7.65	5.85	500 Reg	395	5	1x40 REG	
156	Pantry Presidencia	17,85	5.1	3.5	200	244	3	2X17	
157	SS Presidencia	6,75	3.46	1.95	100	101	1	1X17	
158	Presidencia	31,47	7.25	3.5	300	336	3	3X17	
	Pasillo		3.9	1.5	100	103	1	1X17	
159	Secretaria Presidencia sec 1	18,65	5.8	2.25	300	374	2	3X17	
	Secretaria Presidencia sec 2		2.3	1.85	300	427	1	3X17	
160	Circulación Presidencia	6,00	4	1.5	100	101	1	1X17	
161	Tco de Mtto. Talleres.sec 1	103,2	5.9	5.9	300	335	4	3X17	
	Tco de Mtto. Talleres.sec 2		11.8	5.8	300	300	6	3X17	
162	Acceso Individual a Presid.	23,97	3.85	1.12	100	100	2	1X17	
163	Redes	14,73	3.8	3.8	200	220	2	2X17	
164	Circulacion Redes	29,62	12.5	2	100	120	4	1X17	
165	Redes	13,64	3.85	3.5	200	206	2	2X17	
166	Pase de Redes	18,00	8.9	2	200	213	3	2X17	
167	Redes	13,78	3.85	3.6	200	202	2	2X17	
168	Escalera de Redes y Emergencias	29,78					1		1X14 CIRCULAR ADOSADA
169	Parqueo Motos y Ciclos sec1	155,2	9.6	5.85	75	249	6		2X17 ADOS
	Parqueo Motos y Ciclos sec2		17.8	5.5	75	219	9		2X17 ADOS
170	Parqueo Individual	36,73	6.46	5.9	75	235	4		2X17 ADOS
171	Parqueo Individual	35,57	6.46	5.9	75	235	4		2X17 ADOS
172	Parqueo Individual	35,52	6.46	5.9	75	235	4		2X17 ADOS
173	Guardería de Mascotas. Pet	32,86	5.7	5.7	200	207	3		2X17 ADOS
Total		2							

LUMINARIAS A MONTAR	CANT	POT INST WAT
LUMINARIAS RECTAS EMPOTRADAS PARA LAMP LED 1X9 W 115 V	4	40
LUMINARIAS RECTASEMPOTRADAS PARA LAMP LED 1X17 115V	29	551
LUMINARIAS RECTAS EMPOTRDAS PARA LAMP LED 2X17	101	3838
LUMINARIAS RECTAS EMPOTRDAS PARA LAMP LED 3X17	37	2109
LUMINARIAS EMPOTRADAS PARA LAMP LED 1X40 REGULABLE	29	1160
LUMINARIA CIRCULAR EMPOTRADA PARA BOMBILLO FLUORESCENTE AHORRADOR DE 1X22 W 120 V	5	130
LUMINARIAS RECTAS ADOSADAS PARA LAMP LED 2X17	31	1178
LUMINARIA CIRCULAR ADOSADA PARA LAMP LED DE 1X14	3	42
LUMINARIA DECORATIVA PARA ADOSAR CON SENSOR OFF/ON CON LED 14 W 120 V	10	140
TOTAL DE LUMINARIAS	249	9188
		9.19KW